




7117
7116
7115
7114
7113
7112
7111
7110
7109
7108
7107
7106
7105
7104
7103
7102
7101
수위실


F
E
D
C
B
A


F (2.3)
E (2.2)
(1,2)
D
C (0.2)
B (0.1)
A (0.0)
8109
8110
8111
8112
8113
8114
8115
8116
8117
8118
8101
8102
8103
8104
8105
8106
8107
8108
8108-1
현위치

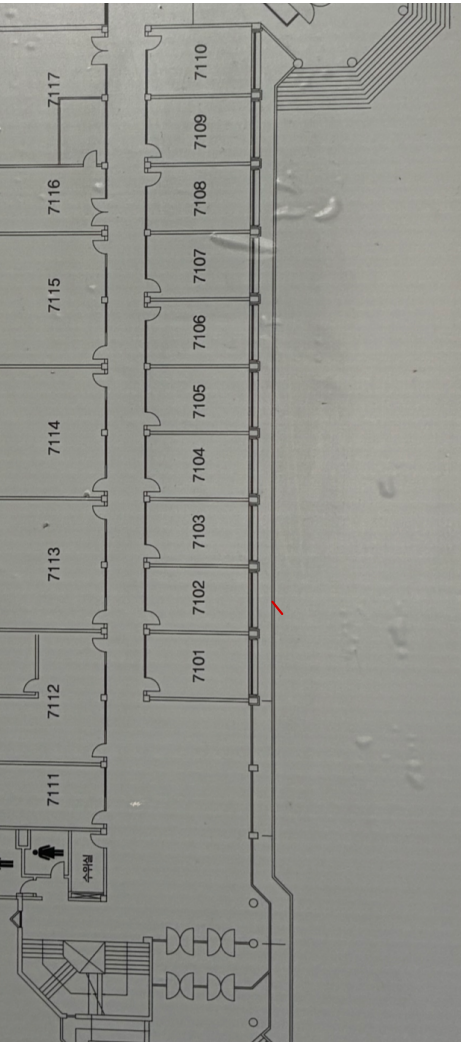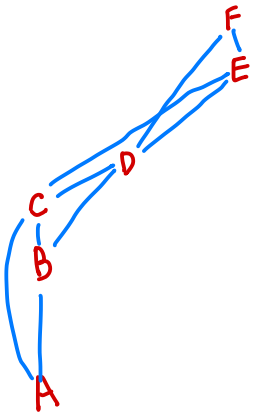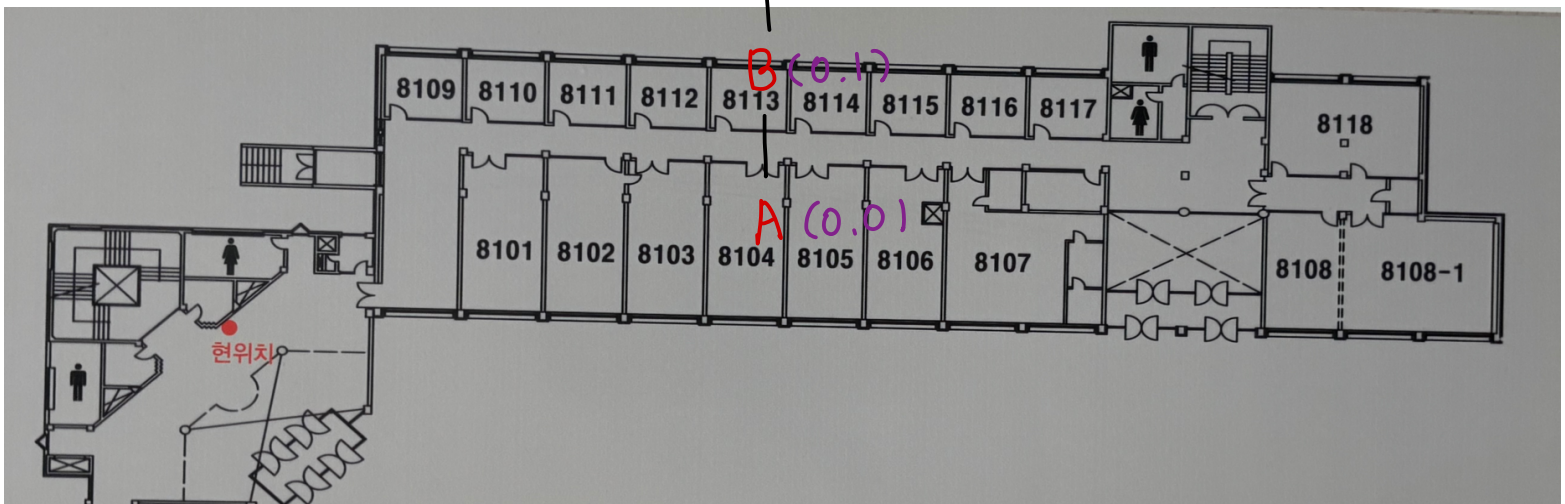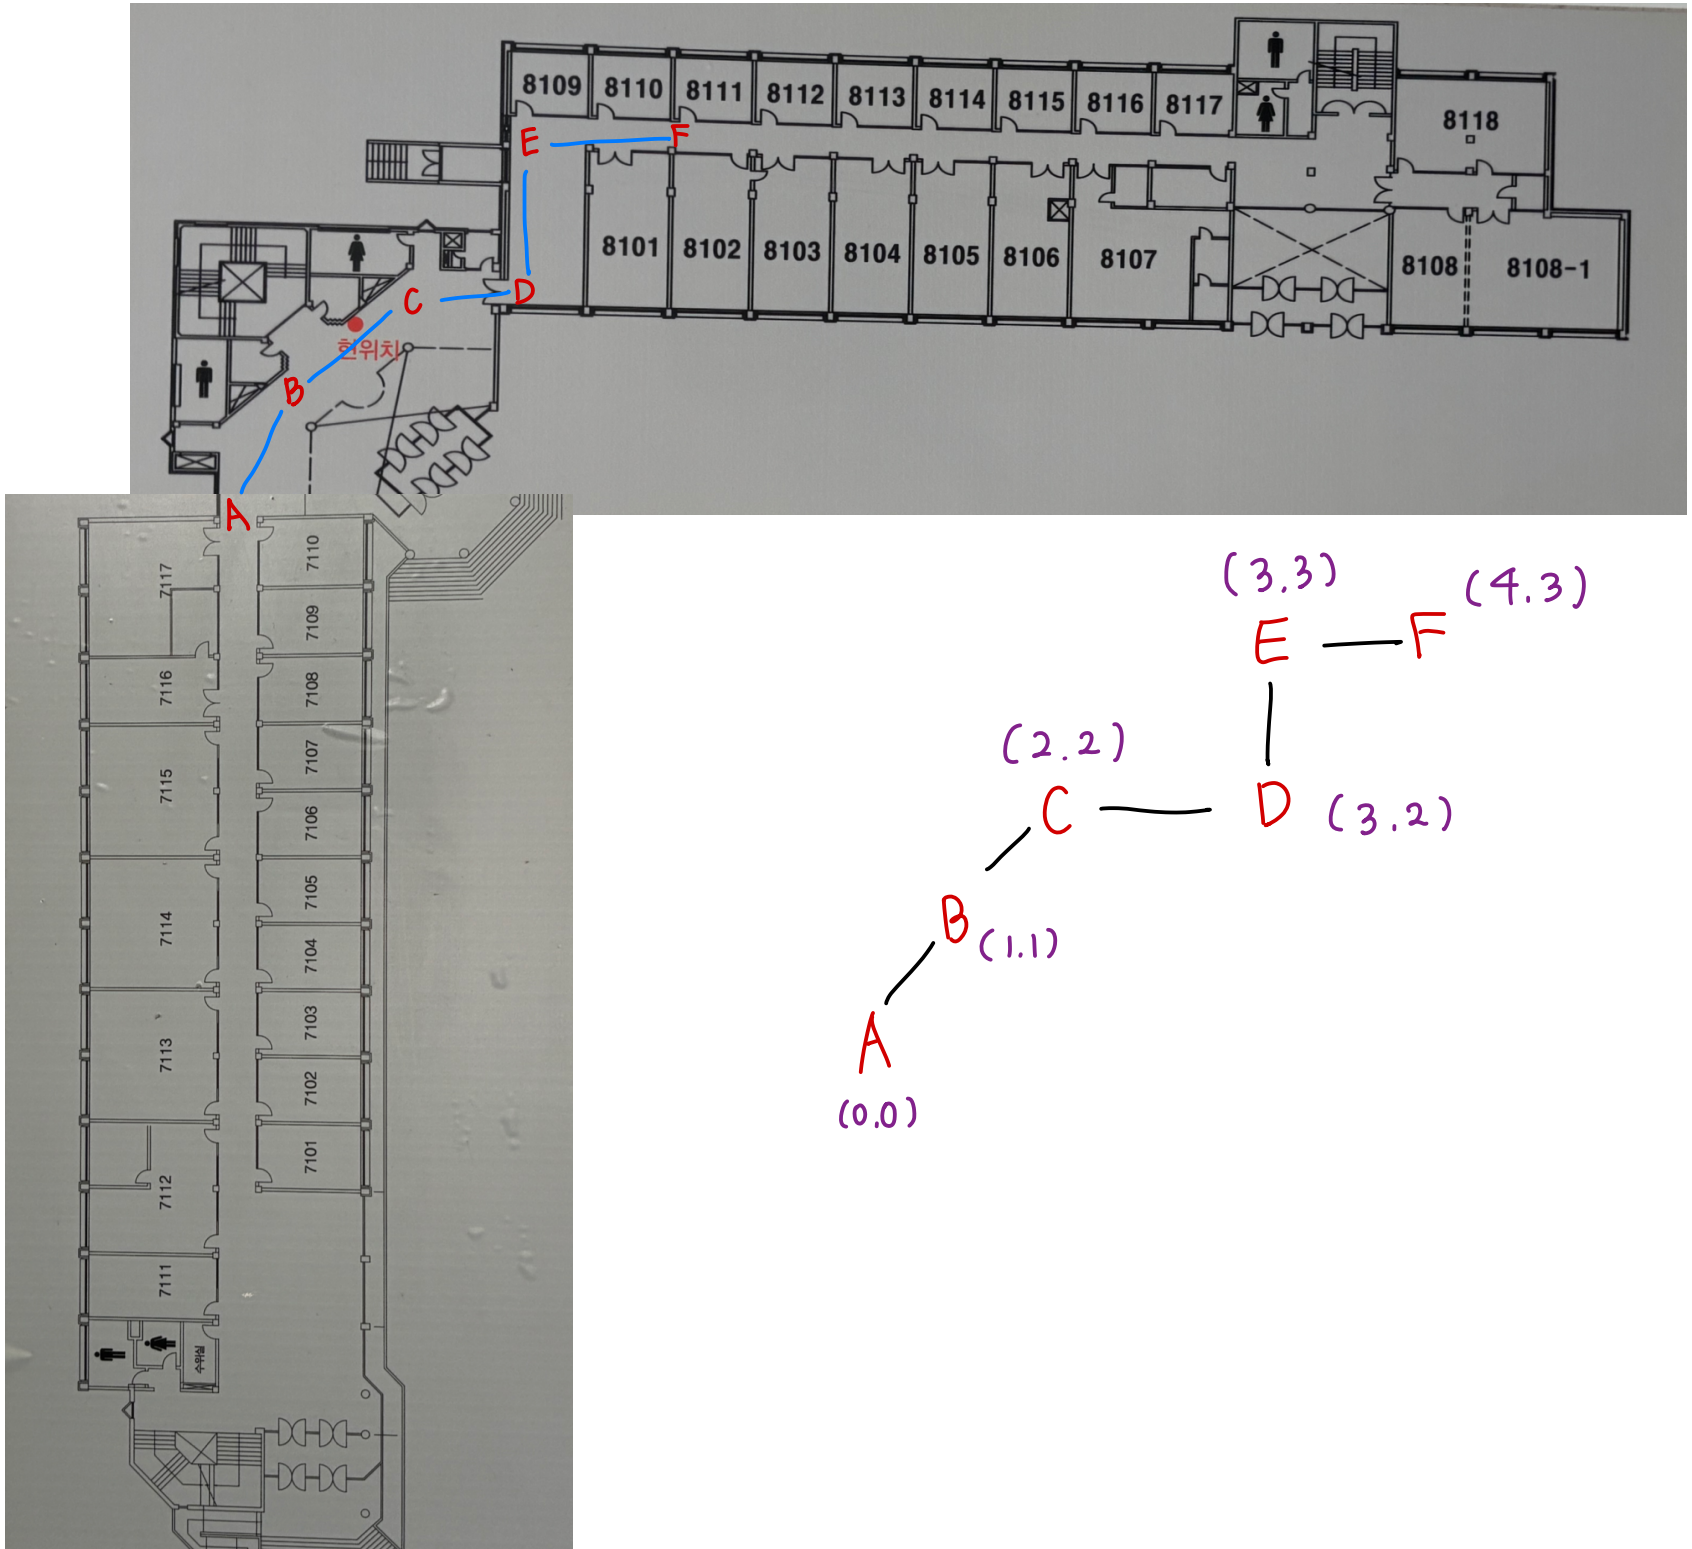

(3,3) (4,3)

E — F


(2,2)


C — D (3,2)


B (1,1)


A


(0,0)

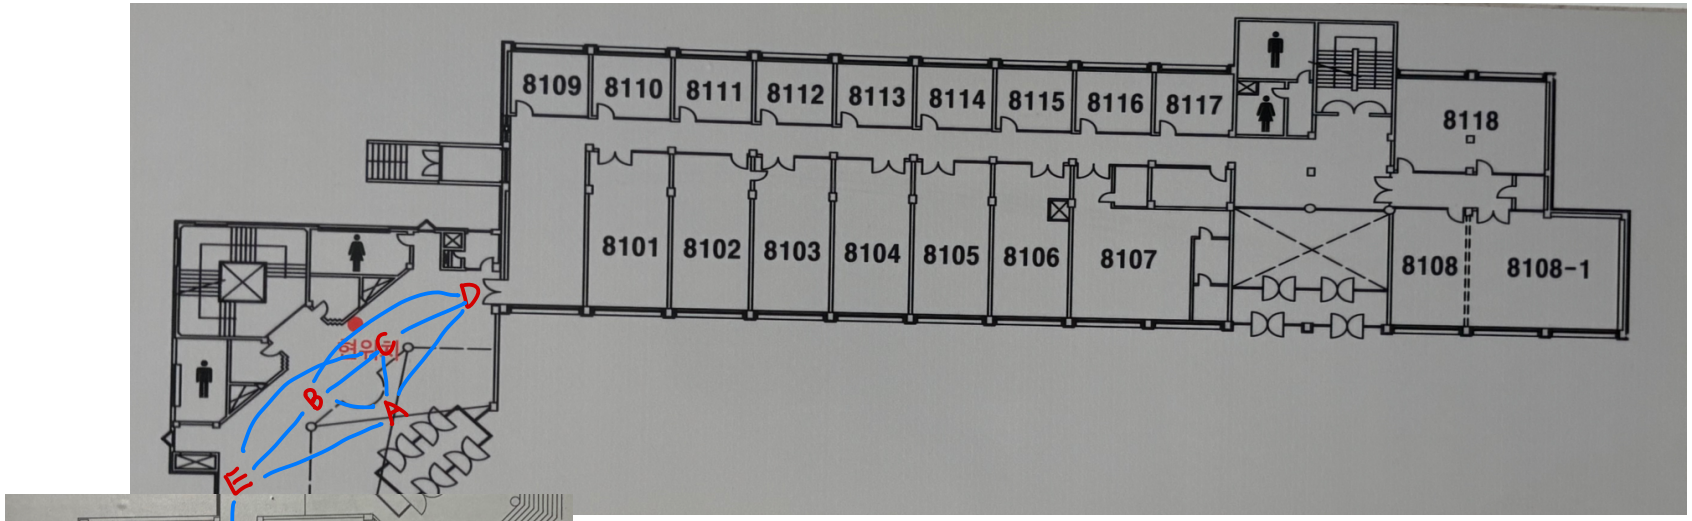

8109
8110
8111
8112
8113
8114
8115
8116
8117
8118
8101
8102
8103
8104
8105
8106
8107
8108
8108-1
D
C
B
A
E
F

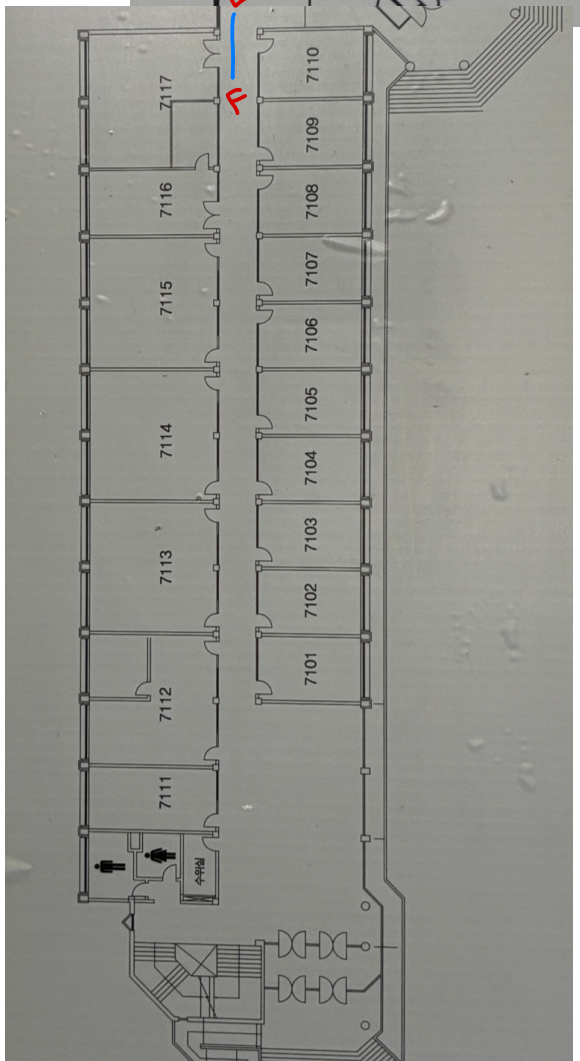

7117
7116
7115
7114
7113
7112
7111
7110
7109
7108
7107
7106
7105
7104
7103
7102
7101

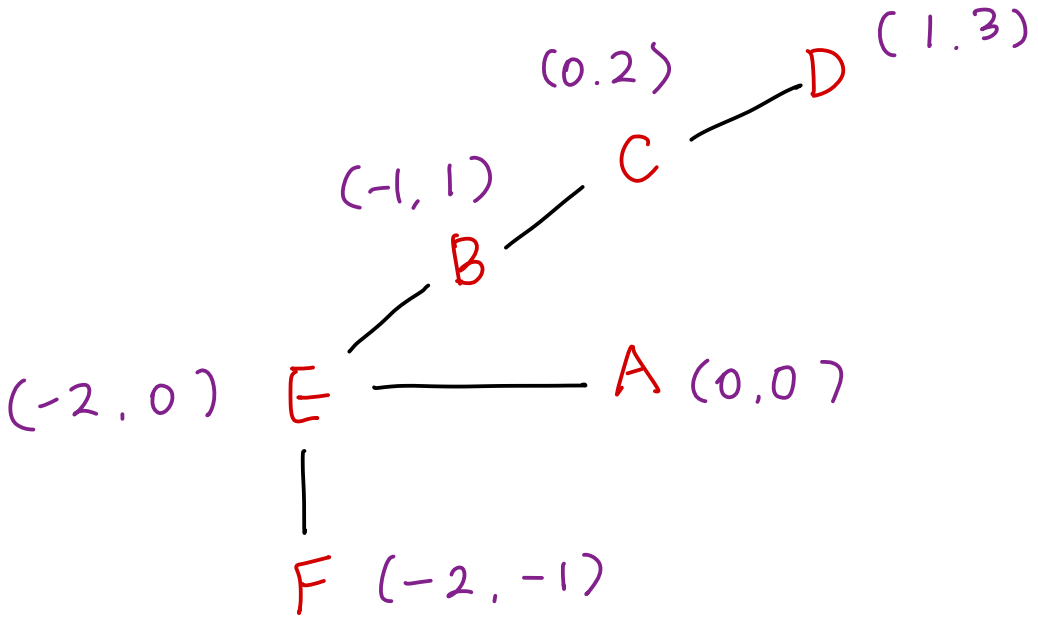
(1,3)
(0,2)
D
C
(-1,1)
B
(-2,0)
E
A
(0,0)
F
(-2,-1)

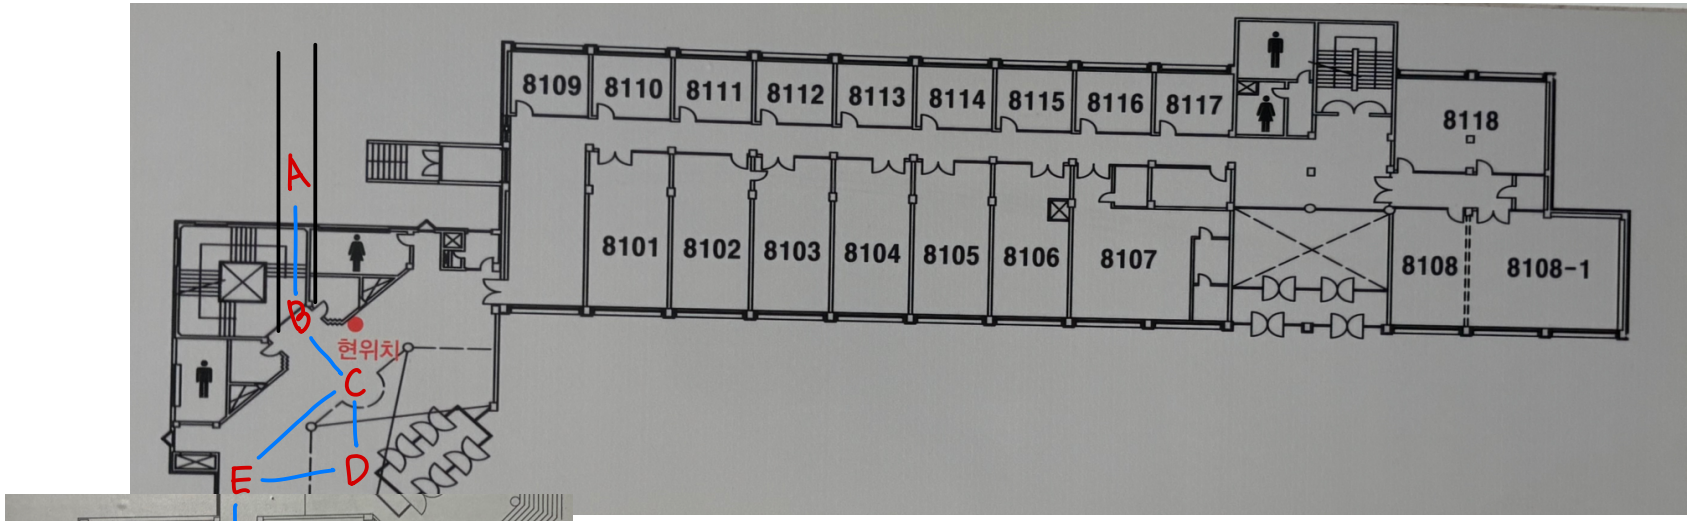
8109
8110
8111
8112
8113
8114
8115
8116
8117
8118
8101
8102
8103
8104
8105
8106
8107
8108
8108-1
A
B
현위치
C
D
E

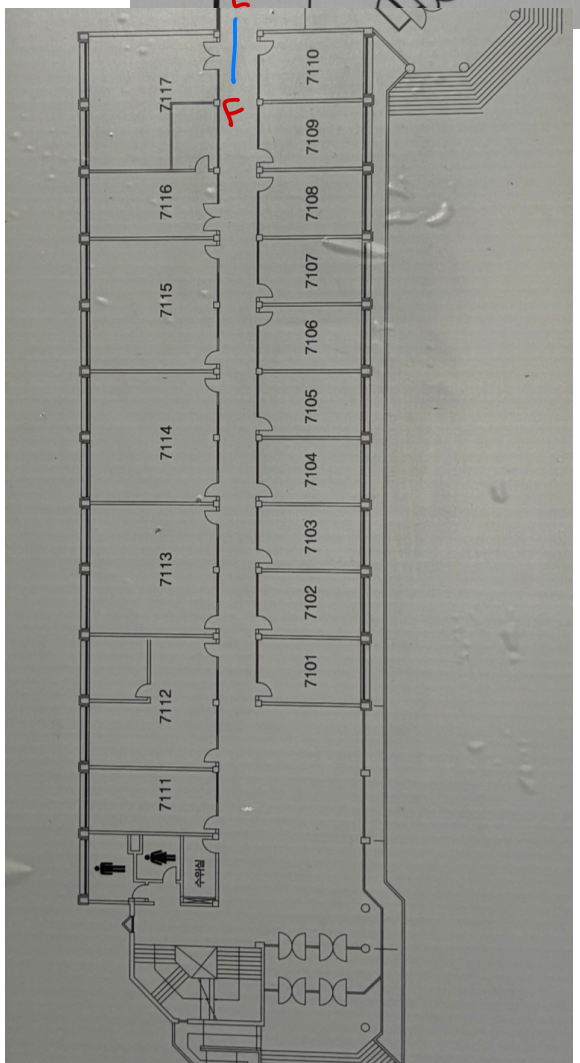
7117
7116
7115
7114
7113
7112
7111
7110
7109
7108
7107
7106
7105
7104
7103
7102
7101
F

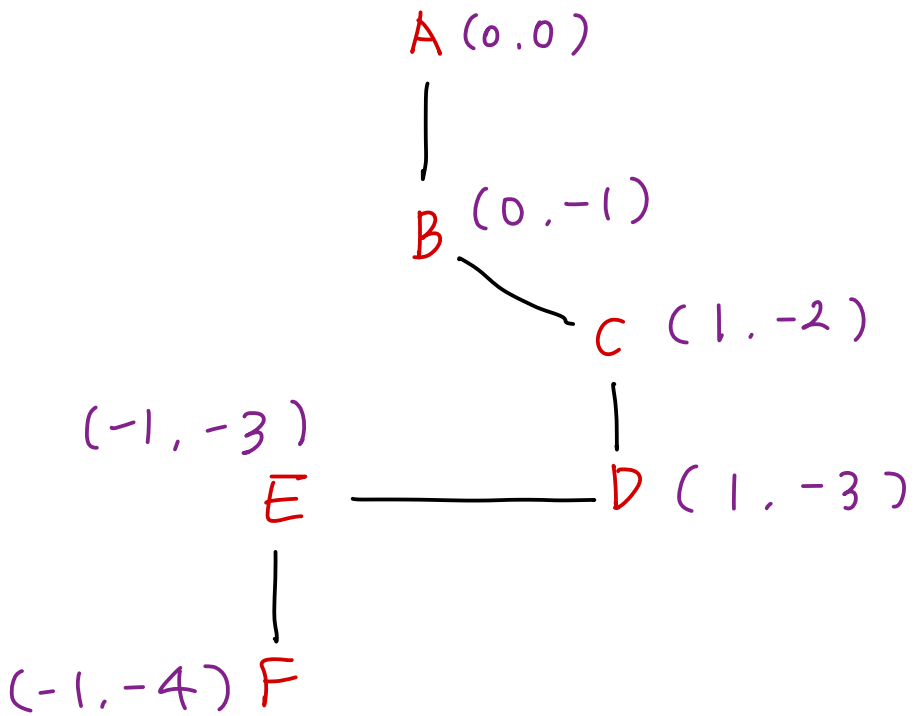
A (0,0)
B (0,-1)
C (1,-2)
(-1,-3)
E
D (1,-3)
(-1,-4) F

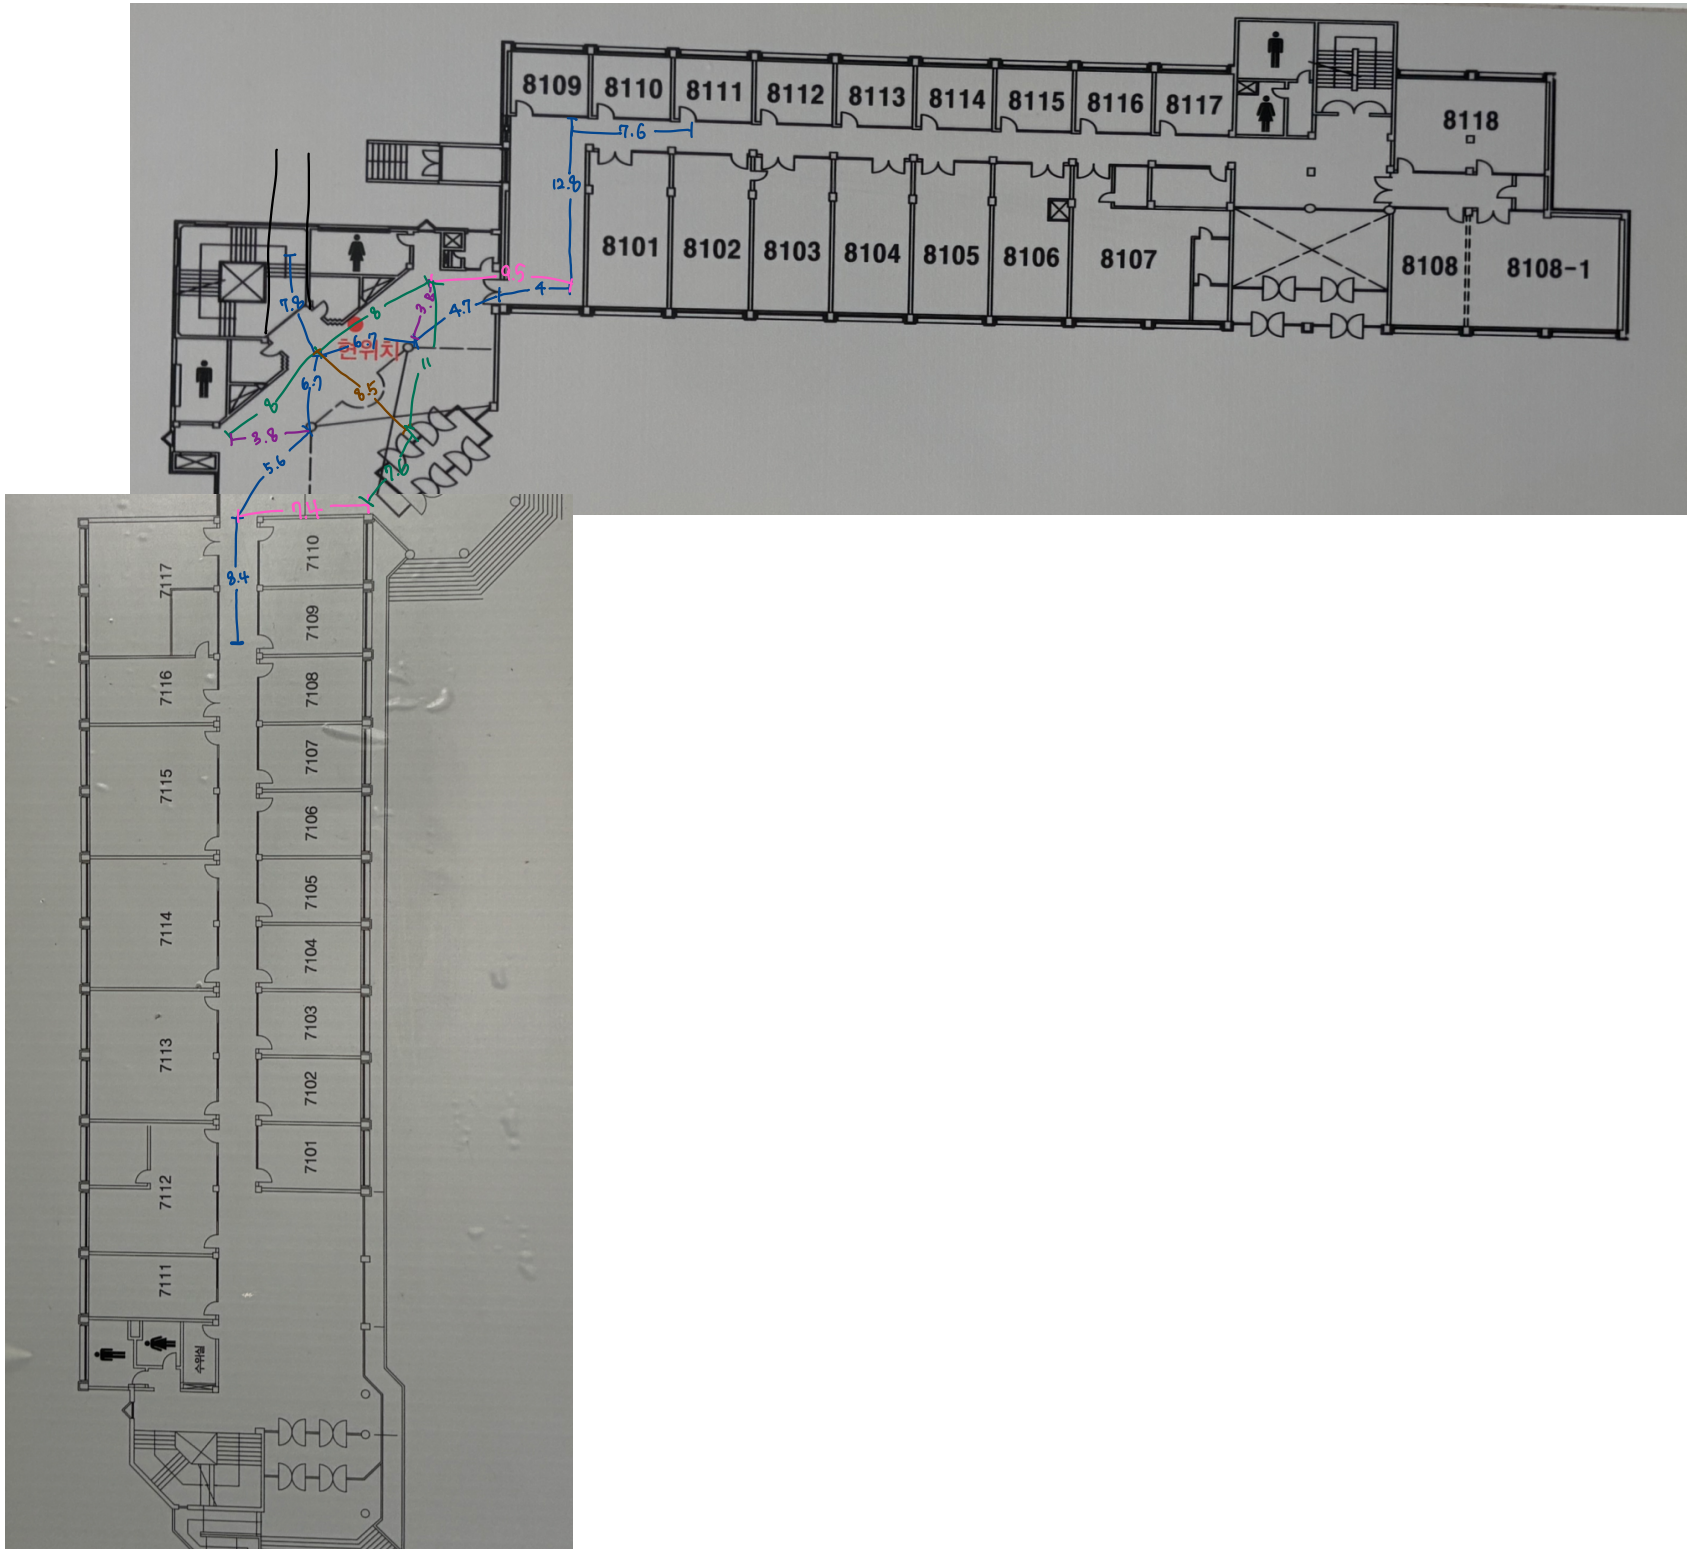

8109
8110
8111
8112
8113
8114
8115
8116
8117
8118
8101
8102
8103
8104
8105
8106
8107
8108
8108-1
7.6
12.8
9.5
4
4.7
3.9
7.8
8
6.7
11
8.5
3.8
5.6
7.4
8.4
콘센트
7117
7116
7115
7114
7113
7112
7111
7110
7109
7108
7107
7106
7105
7104
7103
7102
7101
수위실


9/4

161239



8109
8110
8111
8112
8113
8114
8115
8116
8117
8118
8101
8102
8103
8104
8105
8106
8107
8108
8108-1
F
E
D
C
B
A
7.6
12.3
7.8
8
3.8
4.7
6.7
8
3.8
5.6
8.4
근위치
7117
7116
7115
7114
7113
7112
7111
7110
7109
7108
7107
7106
7105
7104
7103
7102
7101
수위실

162245

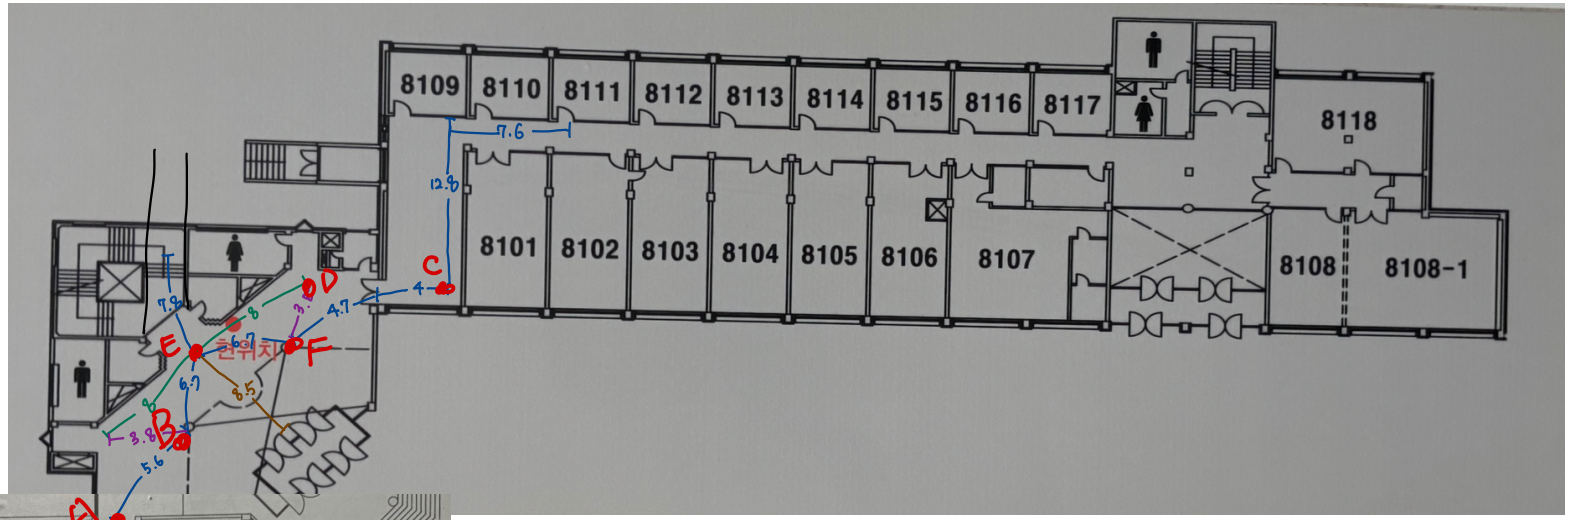

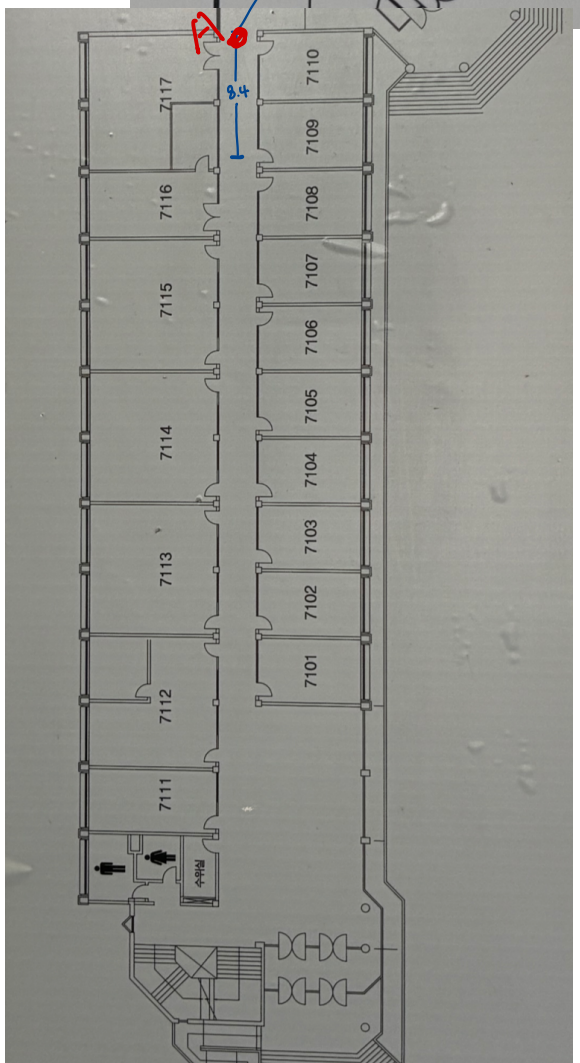



* BF 기둥 → 통신 X
  CF 천장/벽 → 거의 X

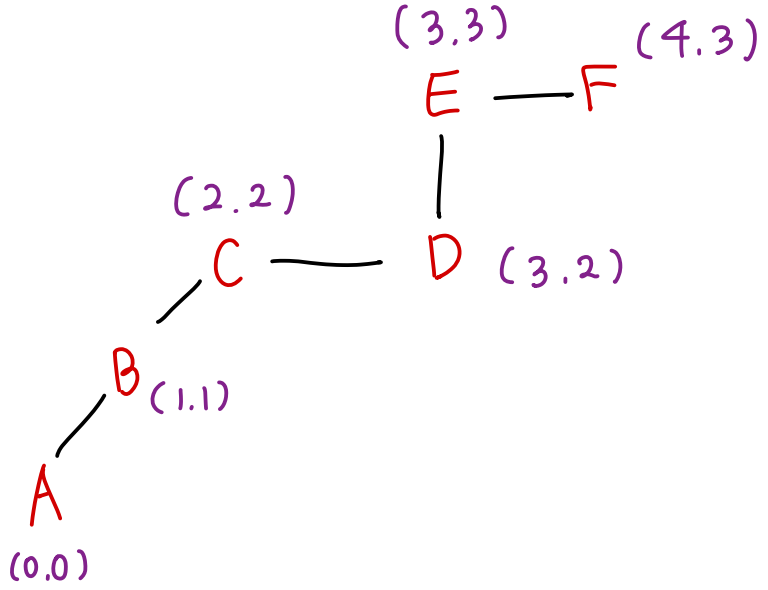


162933


* BF, CF, CE, BE
→ 가능 → 통신X

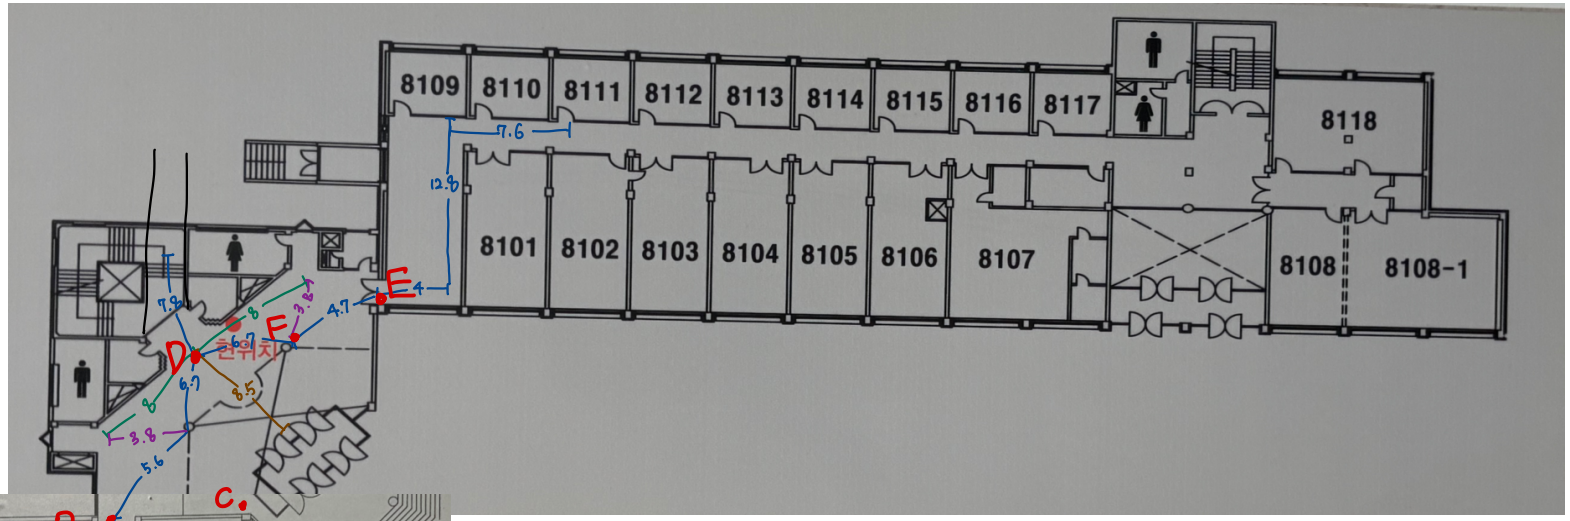


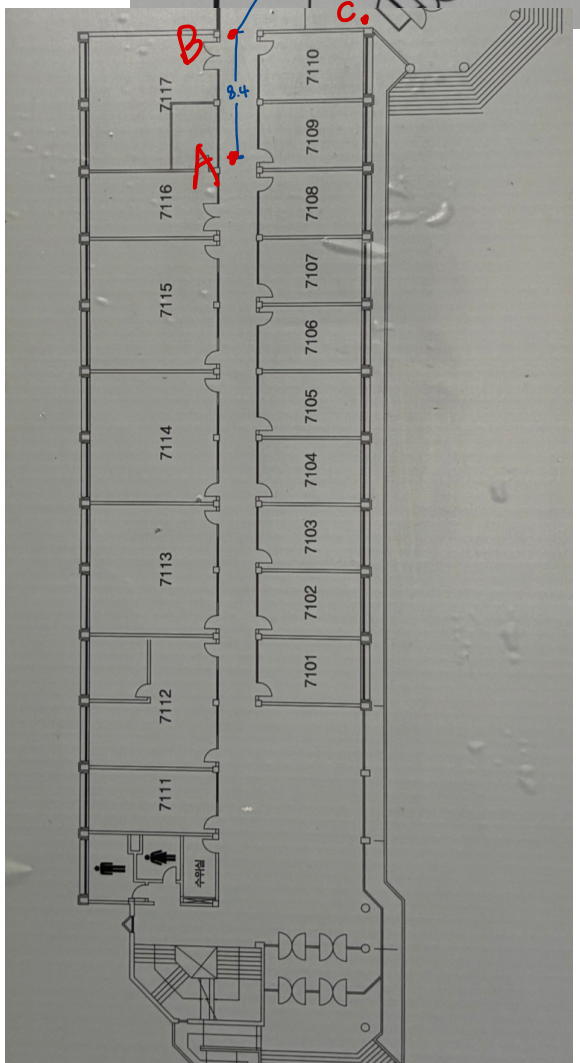

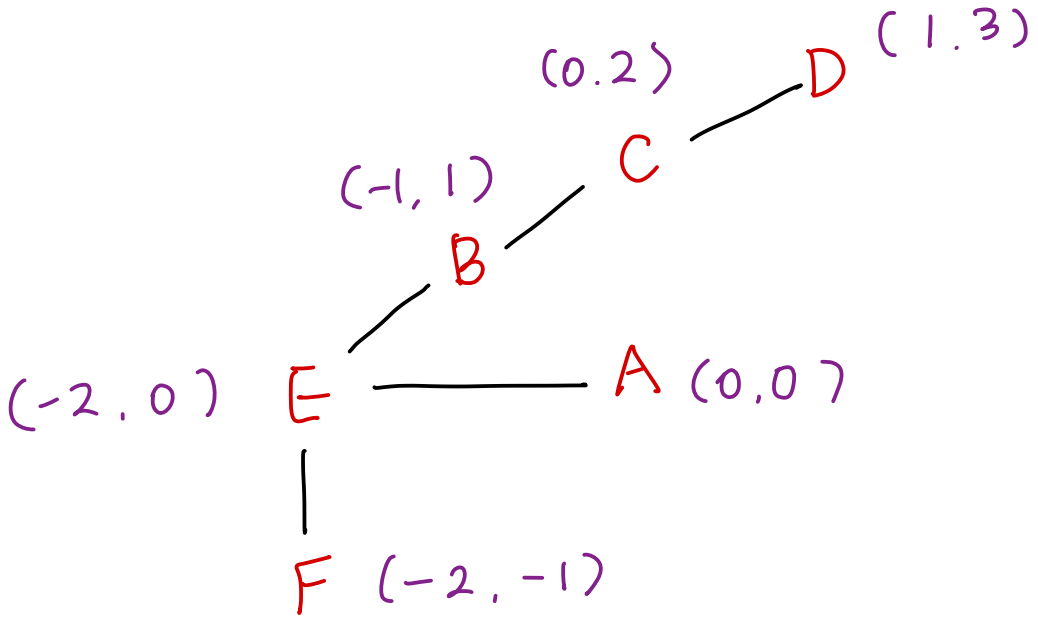

163929

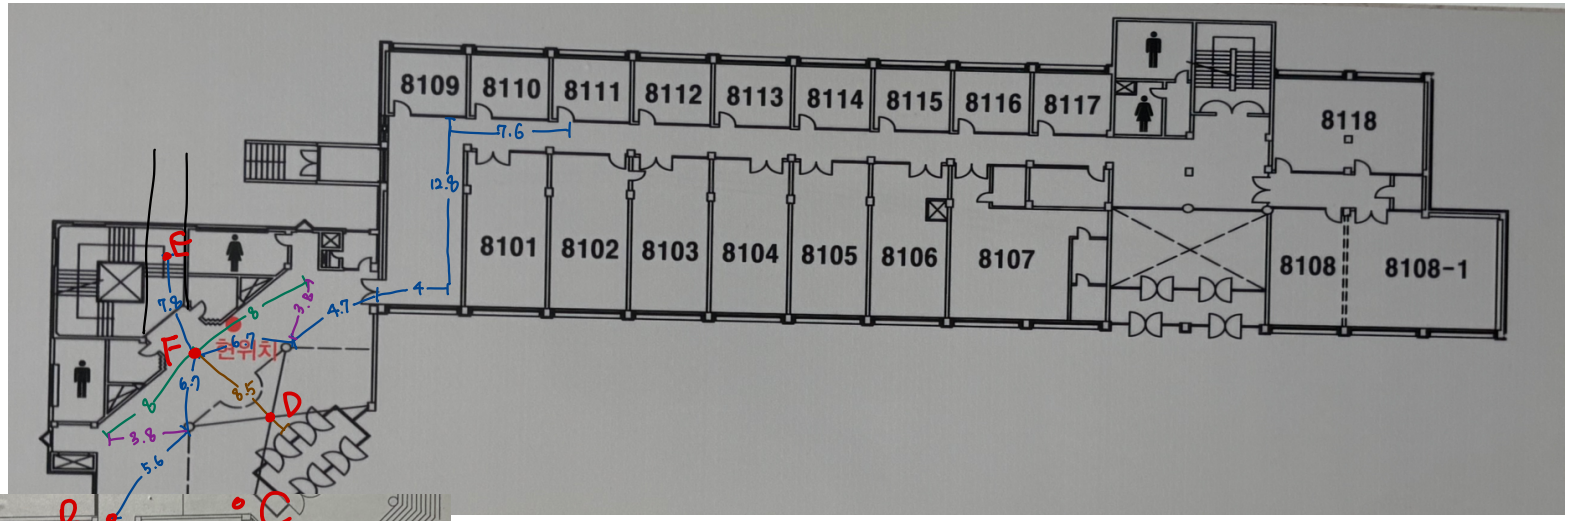

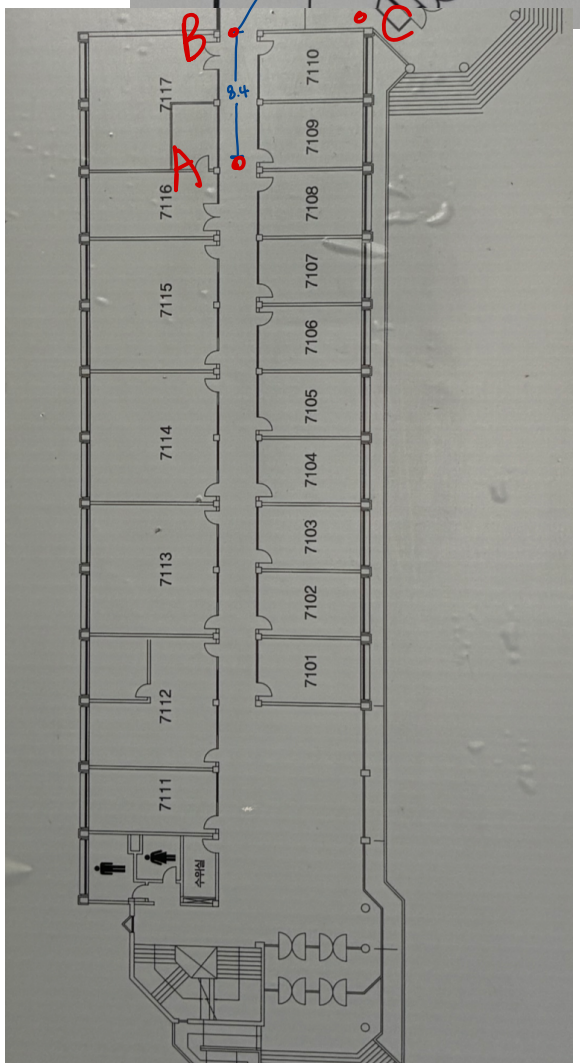

A (0,0)


B (0,-1)

C (1,-2)

D (1,-3)

(-1,-3) E

(-1,-4) F

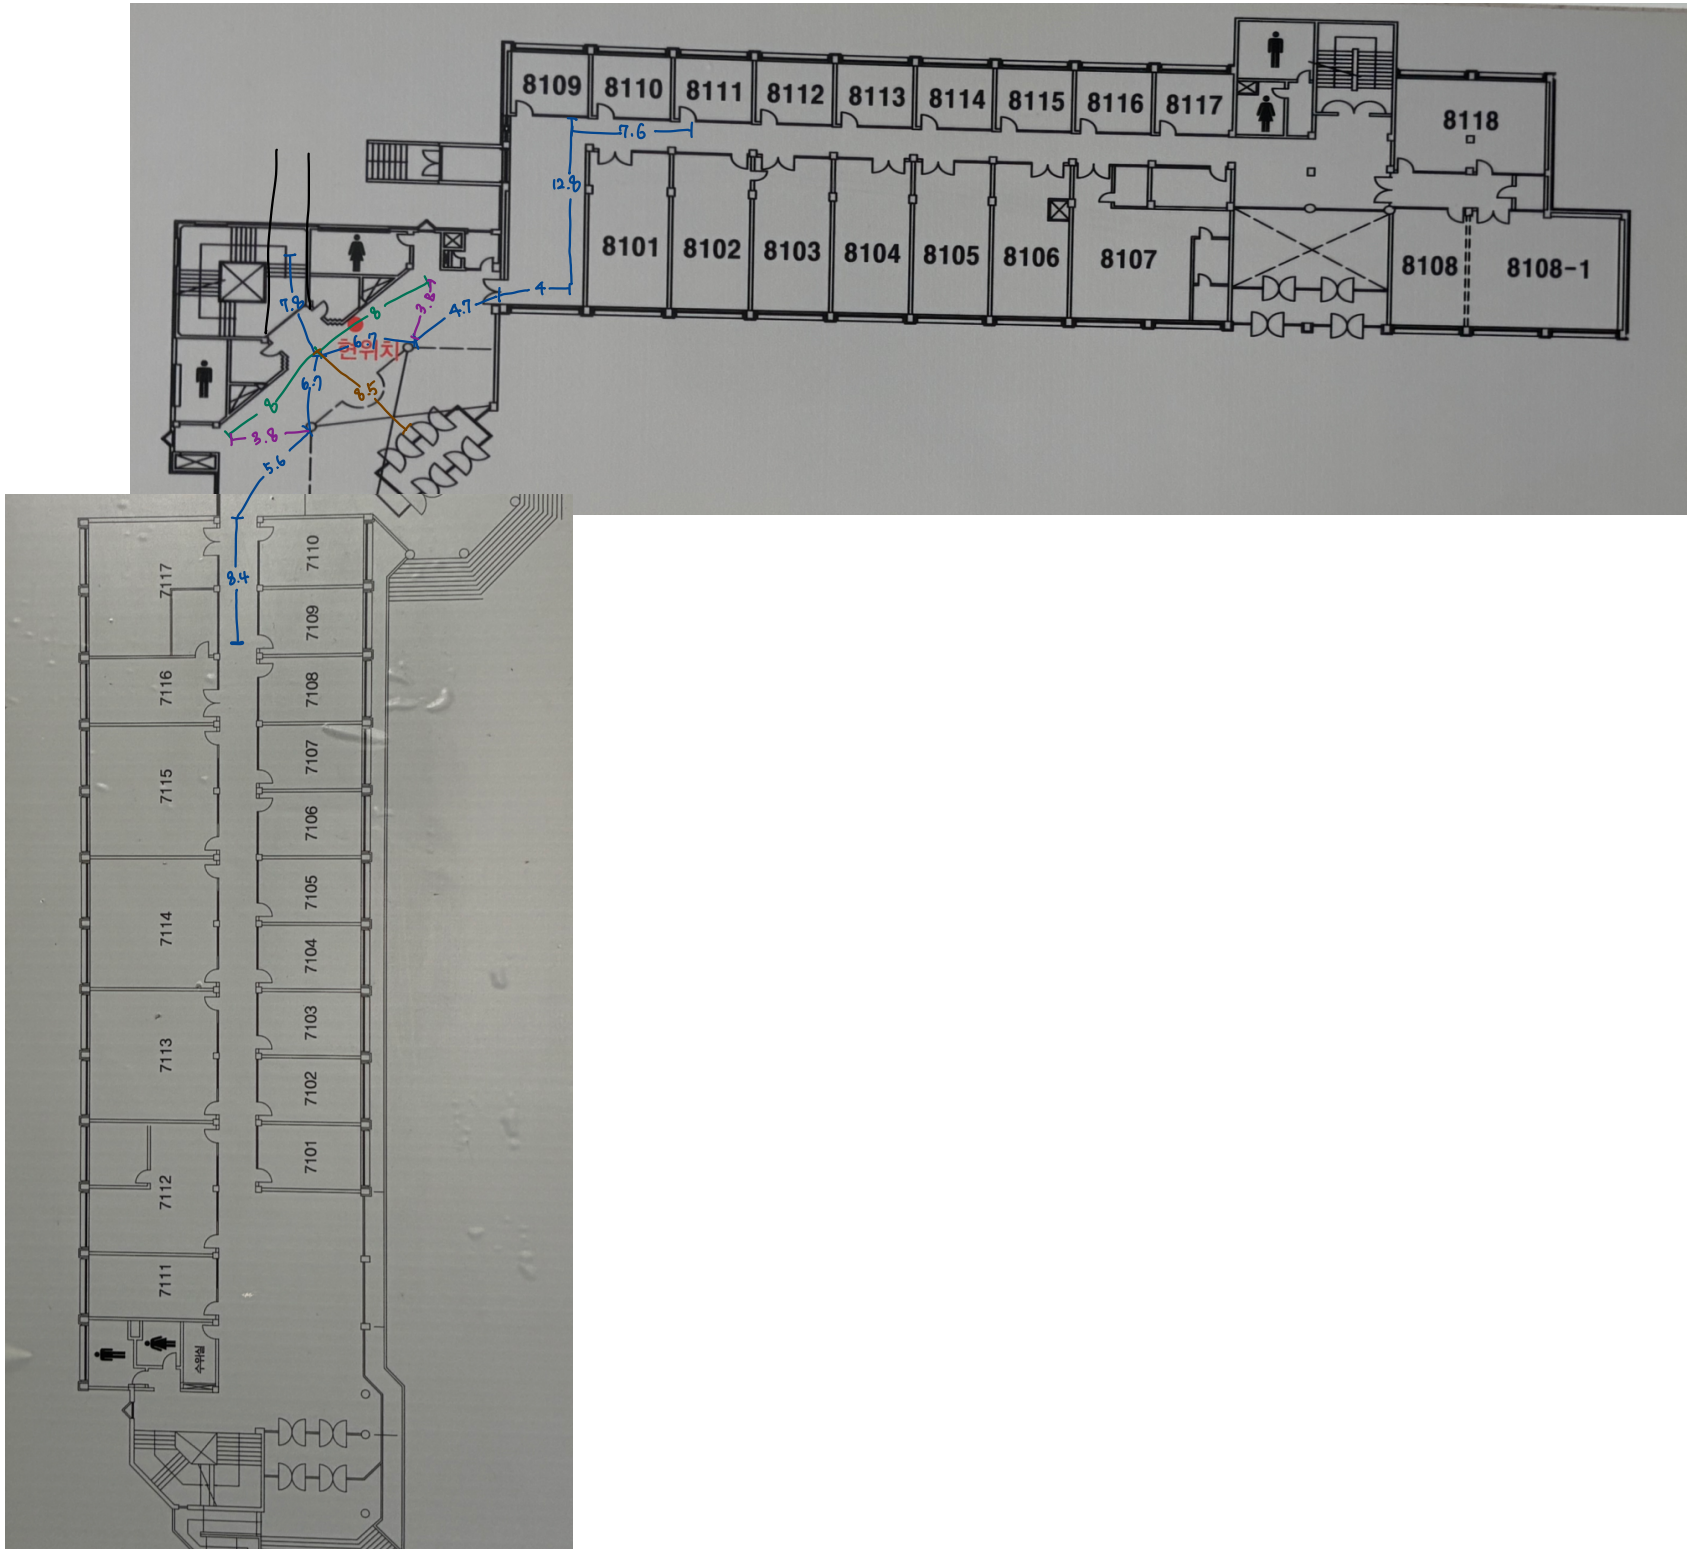
8109
8110
8111
8112
8113
8114
8115
8116
8117
8118
8101
8102
8103
8104
8105
8106
8107
8108
8108-1
7.6
12.8
4
4.7
3.8
7.8
8
6.7
8.5
3.8
5.6
8.4
7117
7116
7115
7114
7113
7112
7111
7110
7109
7108
7107
7106
7105
7104
7103
7102
7101